




P2 SOUTH BUSINESS PARK

HISTORIC DIRIYAH | DIRIYAH I

Concept Stage Design Brief

January, 2025

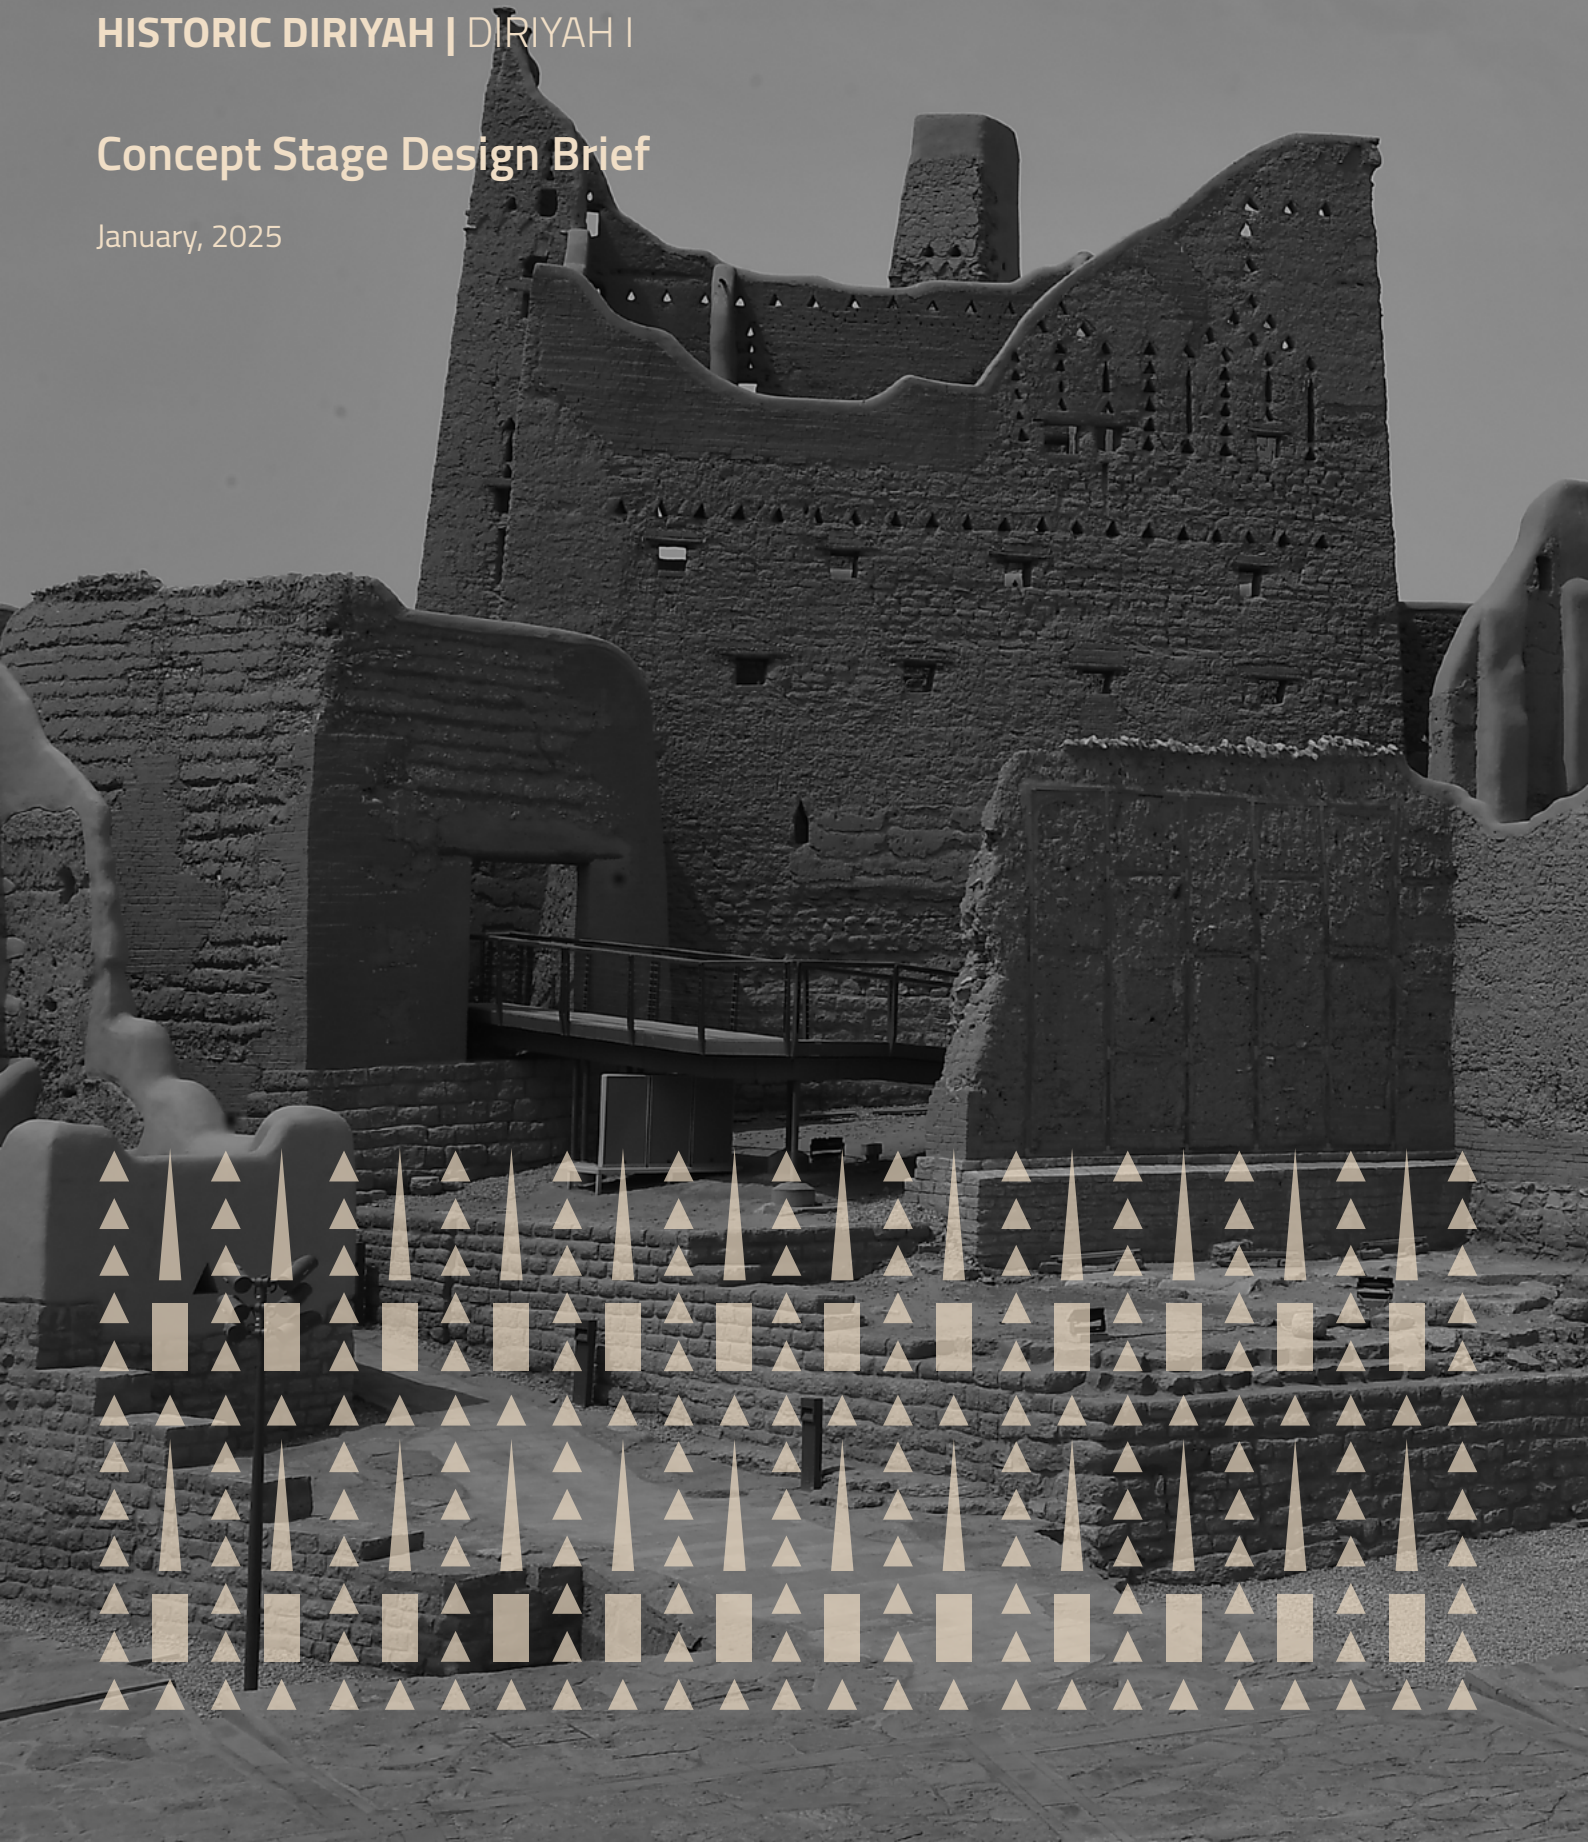



1.0 Introduction	4
1.1 Document Overview	4
1.2 Diriyah Development Company Limited	4
2.0 Master plan Vision and Overview - Diriyah Development	6
2.1 Context	6
2.2 Local Climate	6
2.3 Illustrative Master plan	8
2.4 Master plan Districts	10
2.5 Master plan Design Principles	11
3.0 District Vision and Overview	12
3.1 Events District	12
3.2 Site Access and Connectivity	14
3.3 Bridge and Connectivity	14
3.4 Early Pre-Concept Master Plan of Event District	18
4.0 Design Requirements	22
4.1 General Planning	22
5.0 Above and Below grade Requirements	26
5.1 Introduction	26
5.2 Above Grade Requirements	26
6.0 Design Considerations	33
6.1 Key Considerations	33
6.2 Architectural Language	35
6.3 Vertical Transportation	37
6.4 Structure	37
6.5 Radiant Cooling System	37
6.6 Interior Design	38
6.7 Landscape Design	39
6.8 Sustainability Strategy	40
6.9 Safety & Security Requirements	41
6.10 DC Guidelines	41
7.0 Design Programme & Milestones	42
8.0 Appendix	46
8.1 Definitions	48
8.2 Abbreviations	49
8.3 Project Stakeholders	50
8.4 Consultants Starter Pack	52

1.0 Introduction

1.1 Document Overview

This document is the Design Brief for a Multi-Disciplinary Consultant (MDC) and their supporting design team for the P2 South Business Park, located in the Events district of Historical Diriyah, part of the new Diriyah development in Riyadh, Kingdom of Saudi Arabia.

Above grade assets of the P2 South Business Park will be primarily commercial offices (44,000m²) with F&B and convenience retail (3,000m²) and its associated services all located above a carpark structure (designed by others). The carpark has a capacity of approximately 3,400 bays and designed to serve both Ministry of Culture Head Office and the P2 South Business Park and F&B assets. The offices will be developed on two and three above grade levels (Up to Ground +3).

The ground floor slab of the carpark has been designed to accommodate Grade level loading along the eastern side of the floorplate. The remainder of the floorplate has been designed to accommodate a future Grade + 3 loading.

The MDC team is tasked to provide design services and respond to and challenge the brief and assumptions made to date. Diriyah Company will provide a carpark constraints pack which will provide design limits for the MDC. Prior to proceeding into Concept Design, the consultant will submit after the first two weeks a revised brief based on the consultant findings and early study as the basis for the Concept Design. All design outcomes should achieve the fundamentals set out within this technical document in keeping with the design guidelines and other documentation provided.

The Scope of Work is covered under 2 Tasks (which will be covered under separate Task Orders).

Task 1 is for the above grade office, F&B and public realm above the carpark and the integration of the carpark welcome halls.

Task 2 is for the MoC Pedestrian Bridge connection and its welcome halls.

1.2 Diriyah Company (DC)

Diriyah Development will become the Kingdom's historic and cultural hub, proudly showcasing to the world Saudi Arabia's 300+ years of history through an engaging and inspiring set of heritage, hospitality, education, retail and dining experiences for residents, tourists and frequent visitors.

Diriyah Development will see 14 km² of the historic town of Diriyah transformed into a global tourism destination with its main anchors rooted in its historic culture and heritage. It aims to be developed as an urban, mixed-use development where people can live, work, and visit, inspired by the principles of both new urbanism and historical Najdi architectural typology. Diriyah Gate Development Authority, now Diriyah Company, was established in July 2017 to preserve Diriyah's history, celebrate its community, and create a hub for Saudi Arabian culture and heritage.

DC is focused on protecting and preserving the Kingdom's history including the stories of forefathers as well as the physical heritage, and ensuring Diriyah's cultural landmarks are complimented by leading hospitality brands, fine dining experiences and world-class retail offerings.



2.0 Master Plan Vision & Overview


2.1 Context

Diriyah is easily accessible from the airport and strategically located 15 minutes north-west of the Saudi capital, Riyadh. It is ideally placed to become a historic cultural, lifestyle and tourism hub for the Kingdom. Diriyah is a town located on the north western side of Riyadh. Diriyah – the Jewel of the Kingdom – is home to At-Turaif district, a UNESCO World Heritage Site. It was the epicenter of the movement towards unification of the Arabian Peninsula after a thousand years of fragmentation.

Diriyah is recognized as a symbolic center of inspiration for the generations of leaders that have led the Kingdom since the foundation of the first Saudi Arabian state. Diriyah Development will become a global landmark which will showcase stories of authentic Saudi Arabia.


2.2 Local Climate

Riyadh has a hot desert climate with hot summers and mild winters. The average high temperature in July is 43.6 °C (110.5 °F). And in winter, the daily minimum temperature averages between 8-9 C°. Weather through out the year is mainly dry but receives a fair amount of rain in March and April. The low humidity helps easing the effects of both heat and cold. It is also known to have dust storms during these two months.

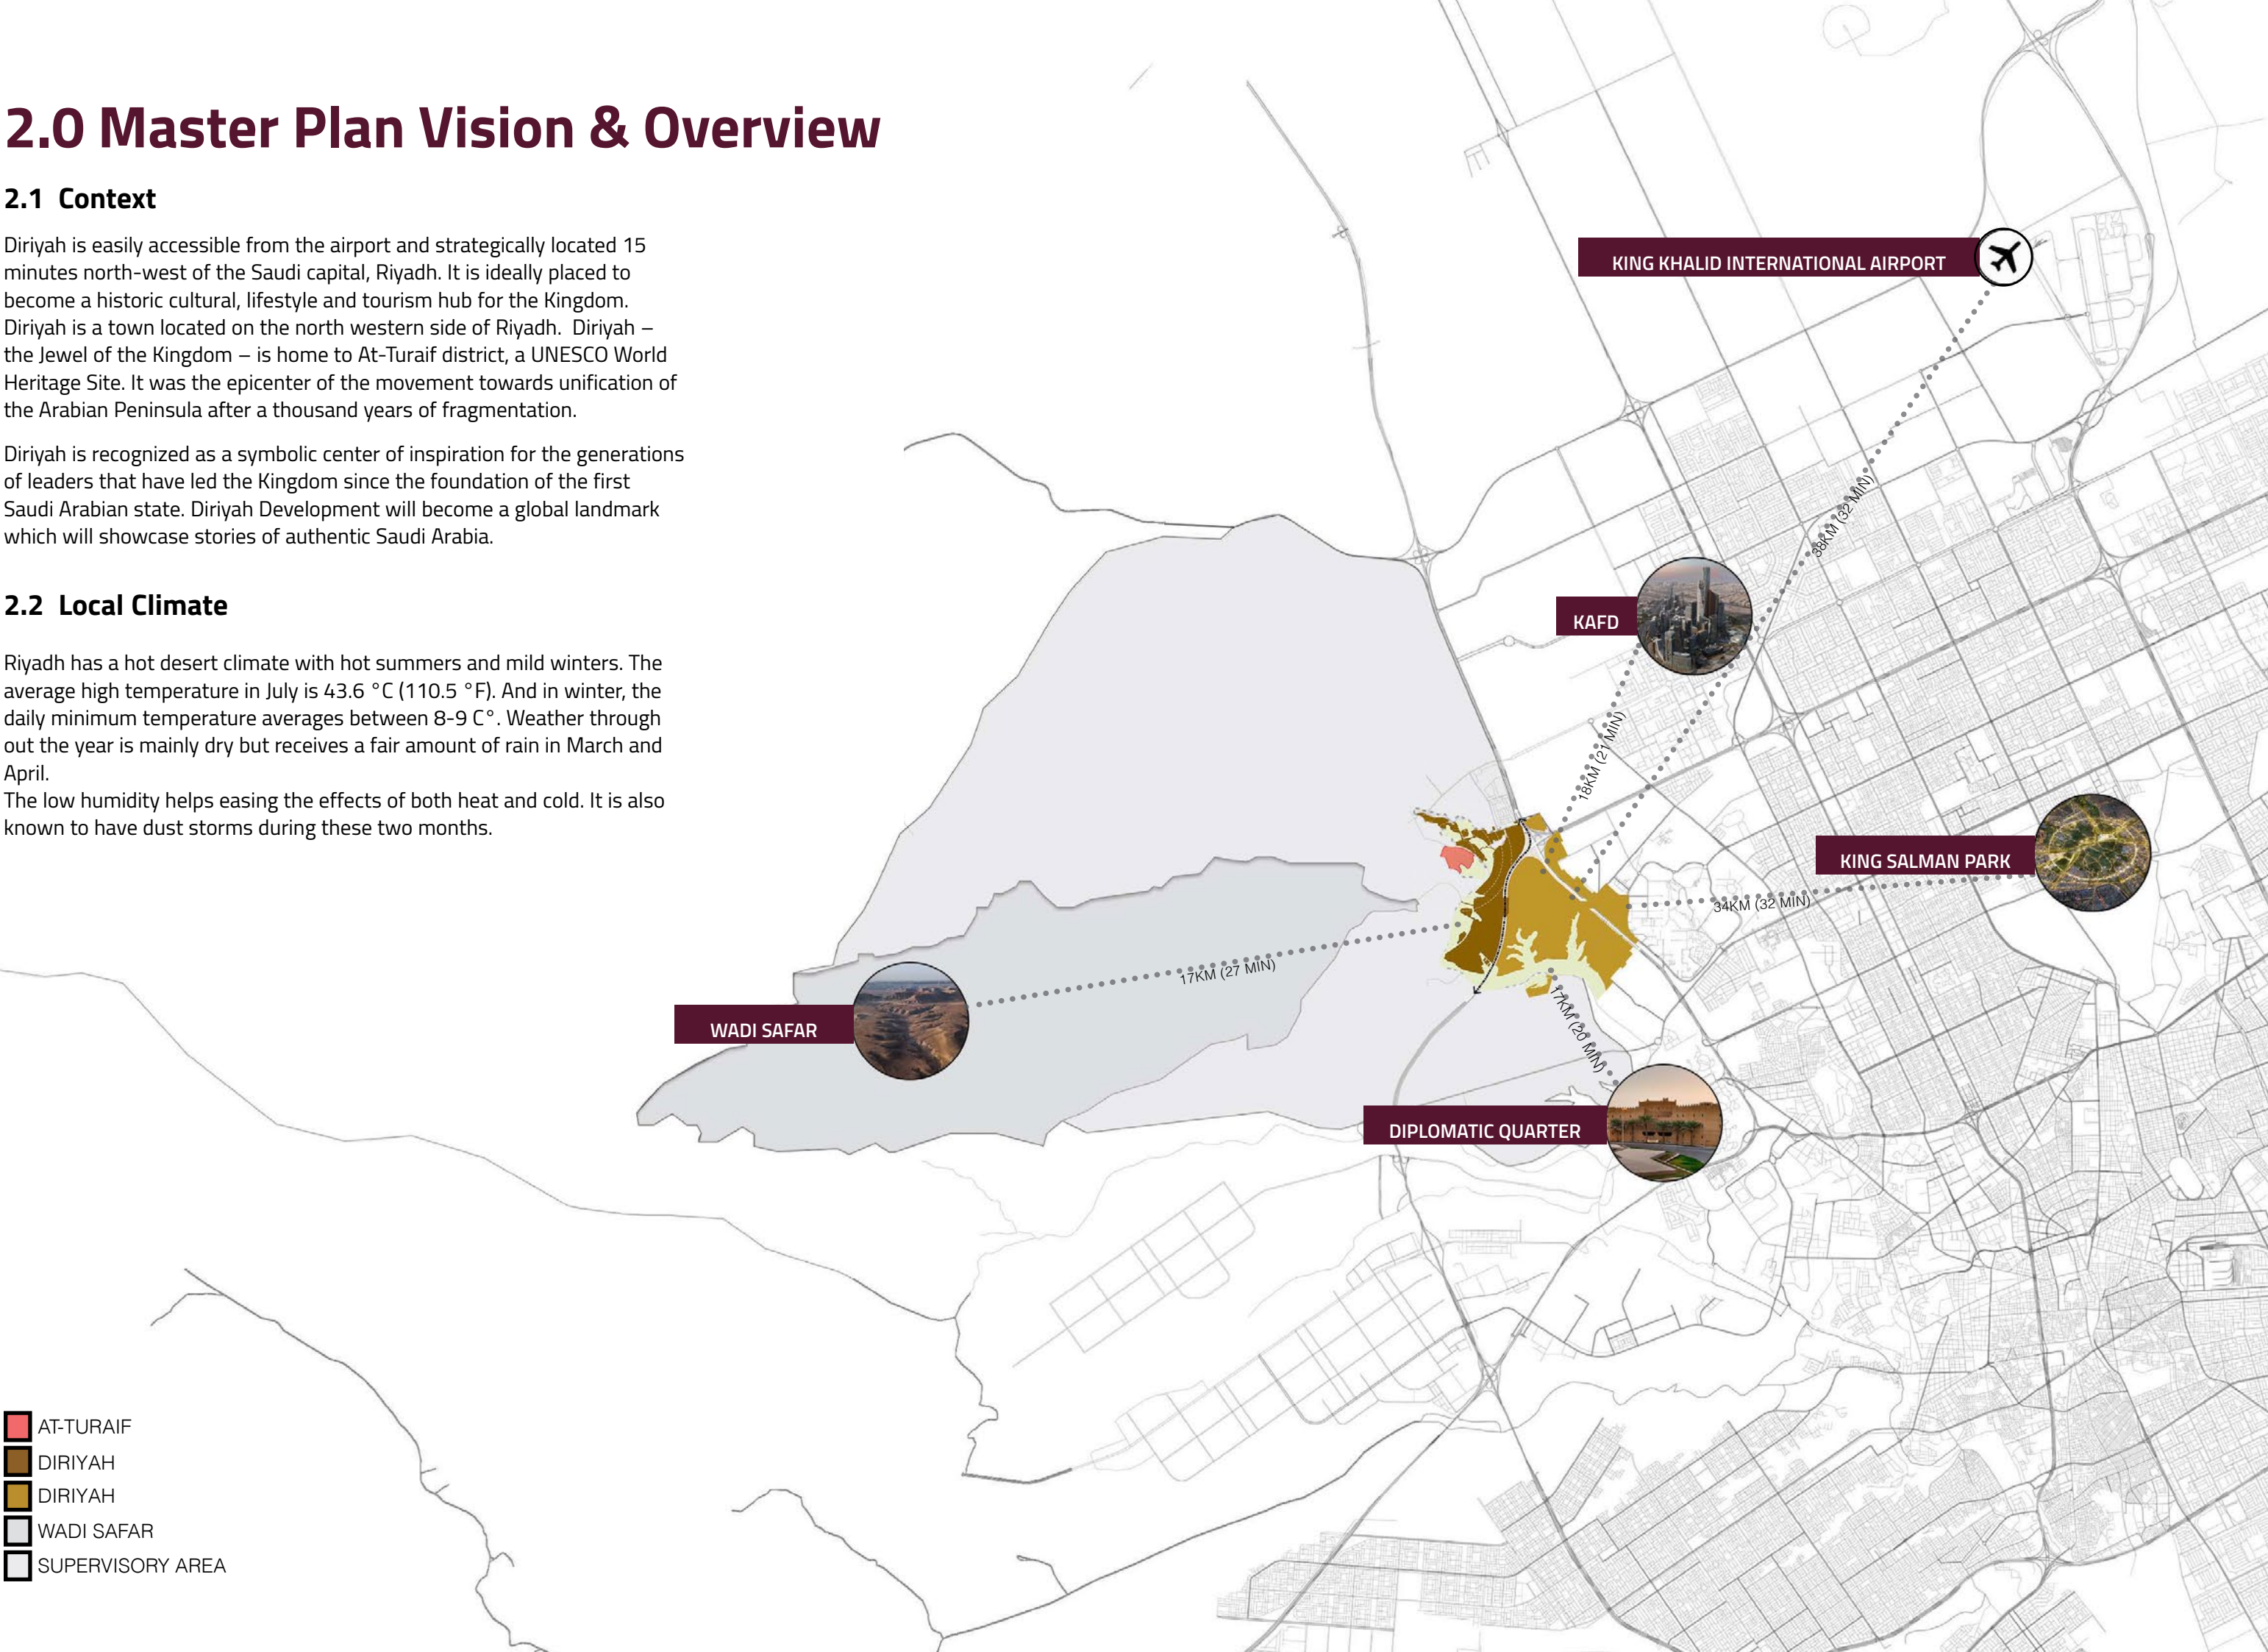



2.4 Master Plan Districts

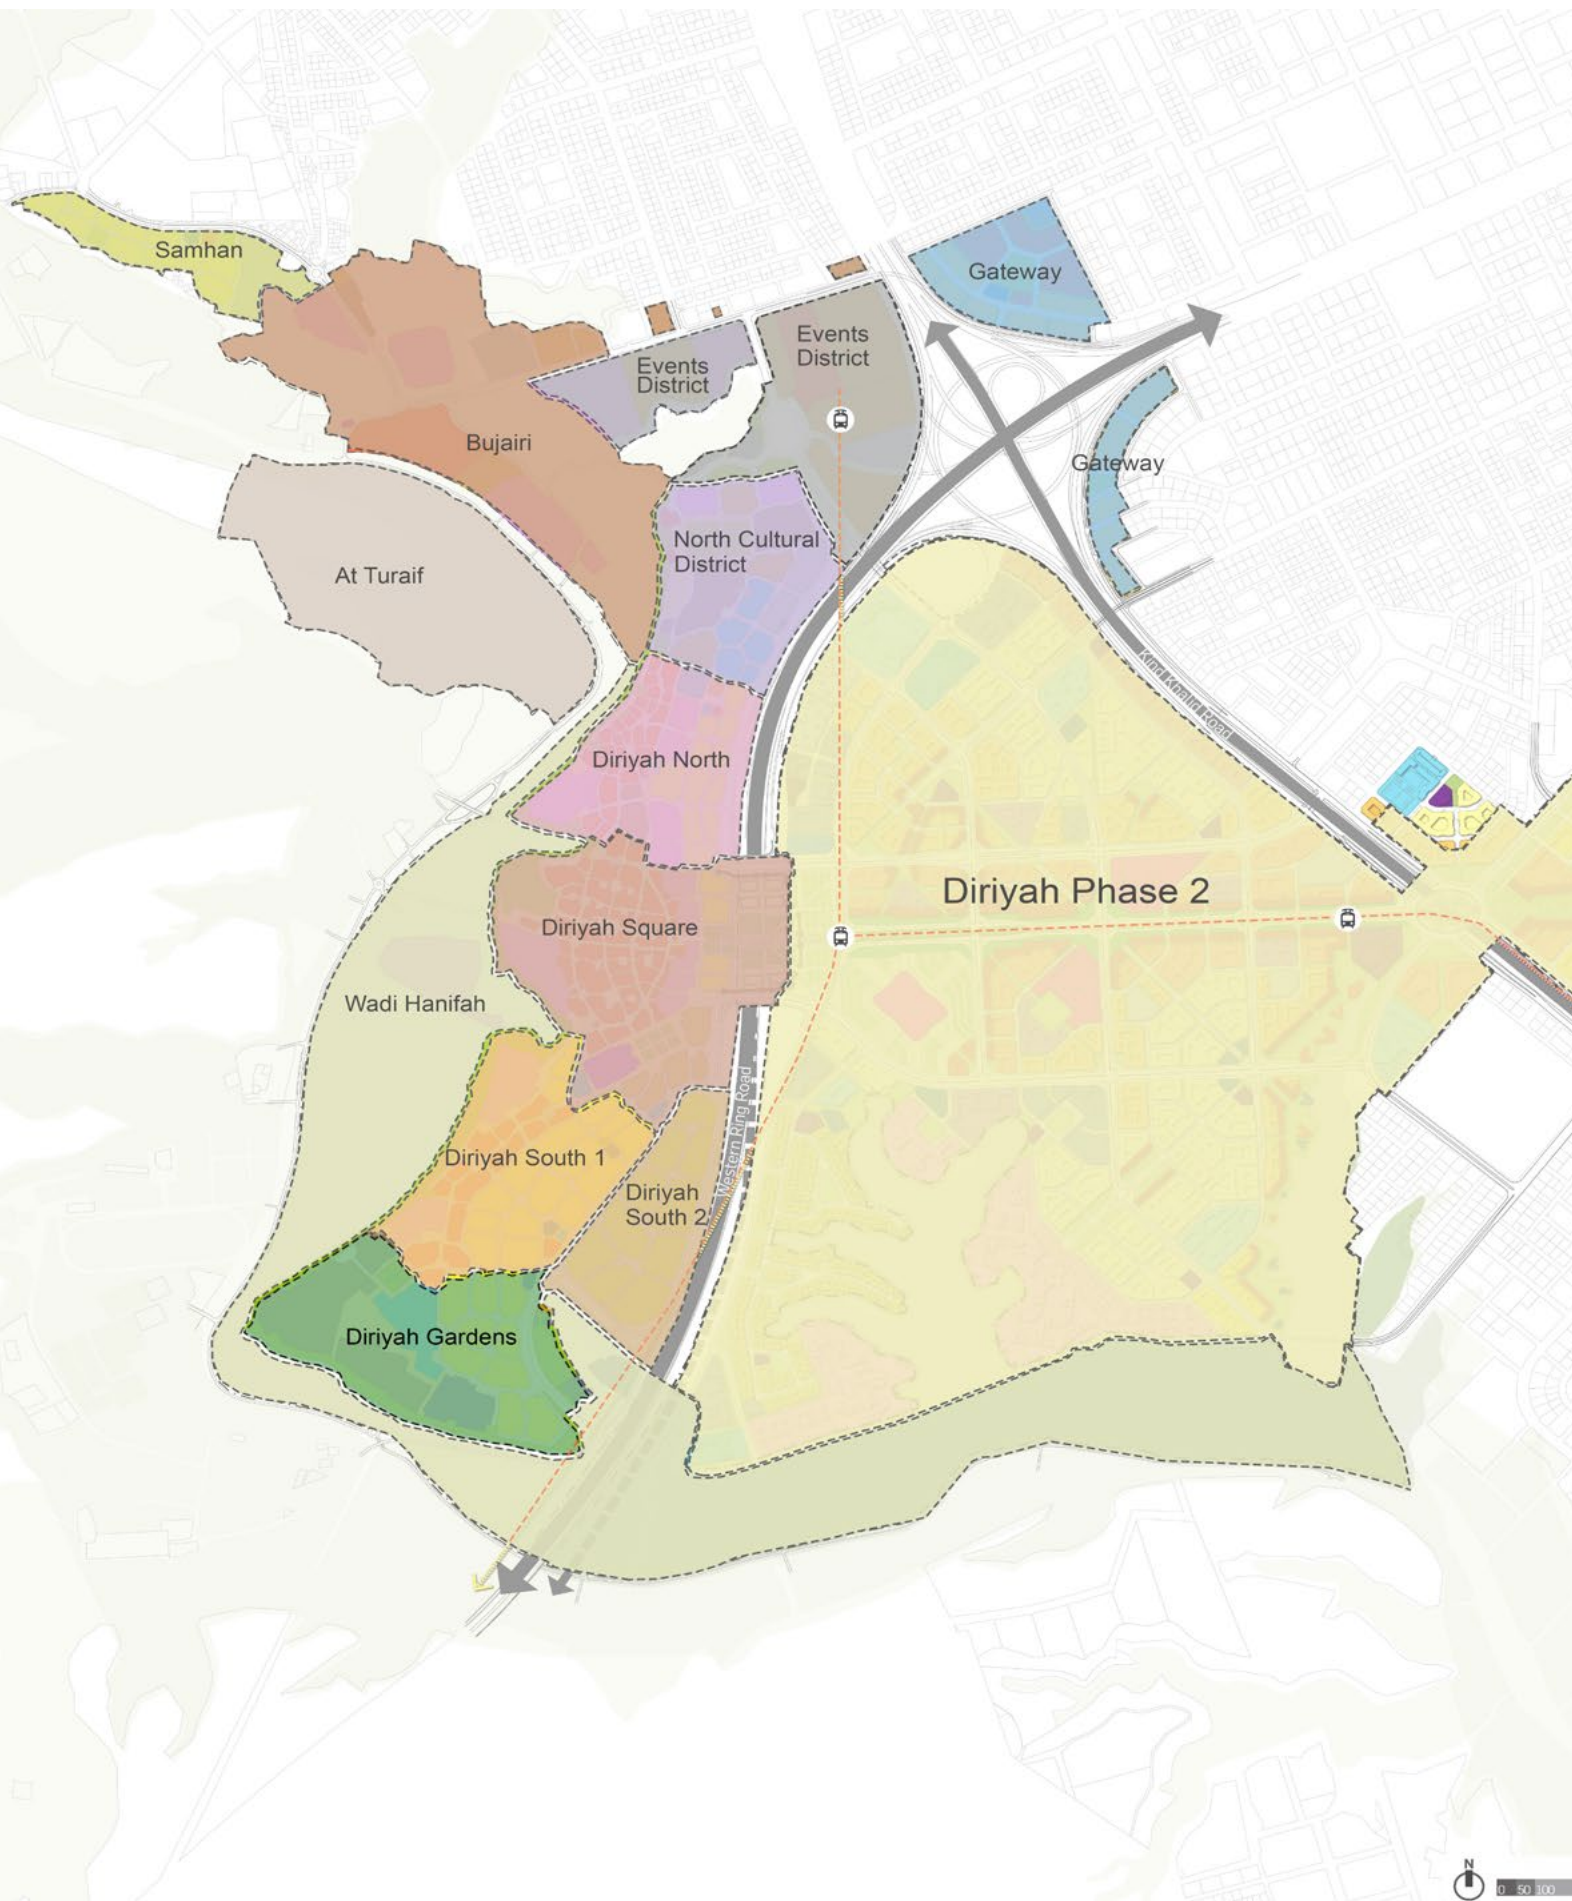

Northern Cultural District:

This district will be well situated near the northern entry point into Diriyah Development and will enjoy close proximity with the large and bustling 'King Salman Square' as well as museums and At-Turaif, the World Heritage Site.

Diriyah North:

This district will be a hub for artistic and cultural ecosystem. It will be located between the northern wadi escarpment edge and the retail district. Meandering streets, laneways and civic plazas provide opportunities to explore and provide the Art District with a sense of traditional Najdi character.

Diriyah Square:

Diriyah Square will be home to leading international luxury lifestyle brands. A completely new lifestyle experience for Saudi Arabia, the retail offering will combine iconic global brands with traditional artisan shops and souks, set within an authentic Najdi village atmosphere.

Diriyah South 1&2:

Situated south of Diriyah Square, Diriyah South provides good views to Wadi Hanifah, hence the urban design strategy has been to maximize open spaces, plazas and active roof-scapes along the escarpment.

Diriyah Gardens:

Planned to accommodate the Museum of Saudi State and the Arabian Peninsula Museum, MISK Museum, Islamic gardens, professional institutions and a number of recreation facilities.*

Gateway Precincts:

Gateway clusters along the main interchange have been planned as Mixed use communities that benefit from good access and frontage opportunities.

Samhan:

Samhan is envisioned to be Najdi residential community overlooking Wadi Hanifah and At-Turaif.

Bujairi:

This district will be developed as a premium dining and lifestyle destination integrated with cultural and entertainment offerings. The district will be surrounded by the panoramic views of the historic At-Turaif the World Heritage Site and Wadi Hanifah.

Events District:

This area is designated for commercial offices, F&B assets and will feature a public realm space and monument that will be flexible and adaptable for a variety of events.

Wadi Hanifah:

Parts of Wadi Hanifah fall within the overall site boundary. The Final Master Plan incorporates the high level zoning strategy from the ongoing landscape Master Plan for Wadi Hanifah by others.

Diriyah Phase 2:

Previously known as Ajmakan North and South, Diriyah Phase 2 is a new development of the Diriyah Gate site.

2.5 Master Plan Design Principles

-  **Walkability:** Most everyday requirements within a short walk along pedestrian friendly streets
-  **Connectivity:** Streets are interconnected through a hierarchy of ways, making walking agreeable and legible
-  **Mixed use and Diversity:** Mixed-use within neighbourhoods with a central focus
-  **Mixed Housing:** A range of types and sizes, in the main fronting the street
-  **Quality Architecture & Urban Design:** Emphasis on traditional beauty and aesthetics, creating a sense of place
-  **Traditional Neighbourhood Structure:** A discernible focus with prominent sites reserved for civic, religious and commercial uses within a short walk
-  **Density:** Buildings, residences, shops and services closer together for ease of walking, to enable a more efficient use of services and resources
-  **Sustainability:** Minimal environmental impact of development, eco and energy friendly technologies, respect for ecology and value of natural systems.


3.0 District Vision & Overview

3.1 Events District

The Events District is the gateway into Diriyah. It is strategically located to welcome visitors and residents to all phases of Diriyah Development. As part of Diriyah I, it forms part of the walkable web of Districts and neighbourhoods, that is well served by public transport with its own dedicated Metro station..

Nearby, at the heart of DGI’s development, the UNESCO’s World Heritage site of At Turaif welcomes visitors and stands as a symbol of Saudi Arabia’s rich history and a sanctuary for national heritage preserved in open-airmuseums.

Salwa Palace is the largest standing structure in the citadel and of significant importance as the home of Kings & Heroes. Also within walking distance is Bujairi Terrace, a world-class food and beverage offering ranging from pit stop coffee shops to leisurely fine-dining experiences as well as a 1400, 4 level underground car park garage. A collection of 18 brands brought together to cater for local and international visitors for the first time.

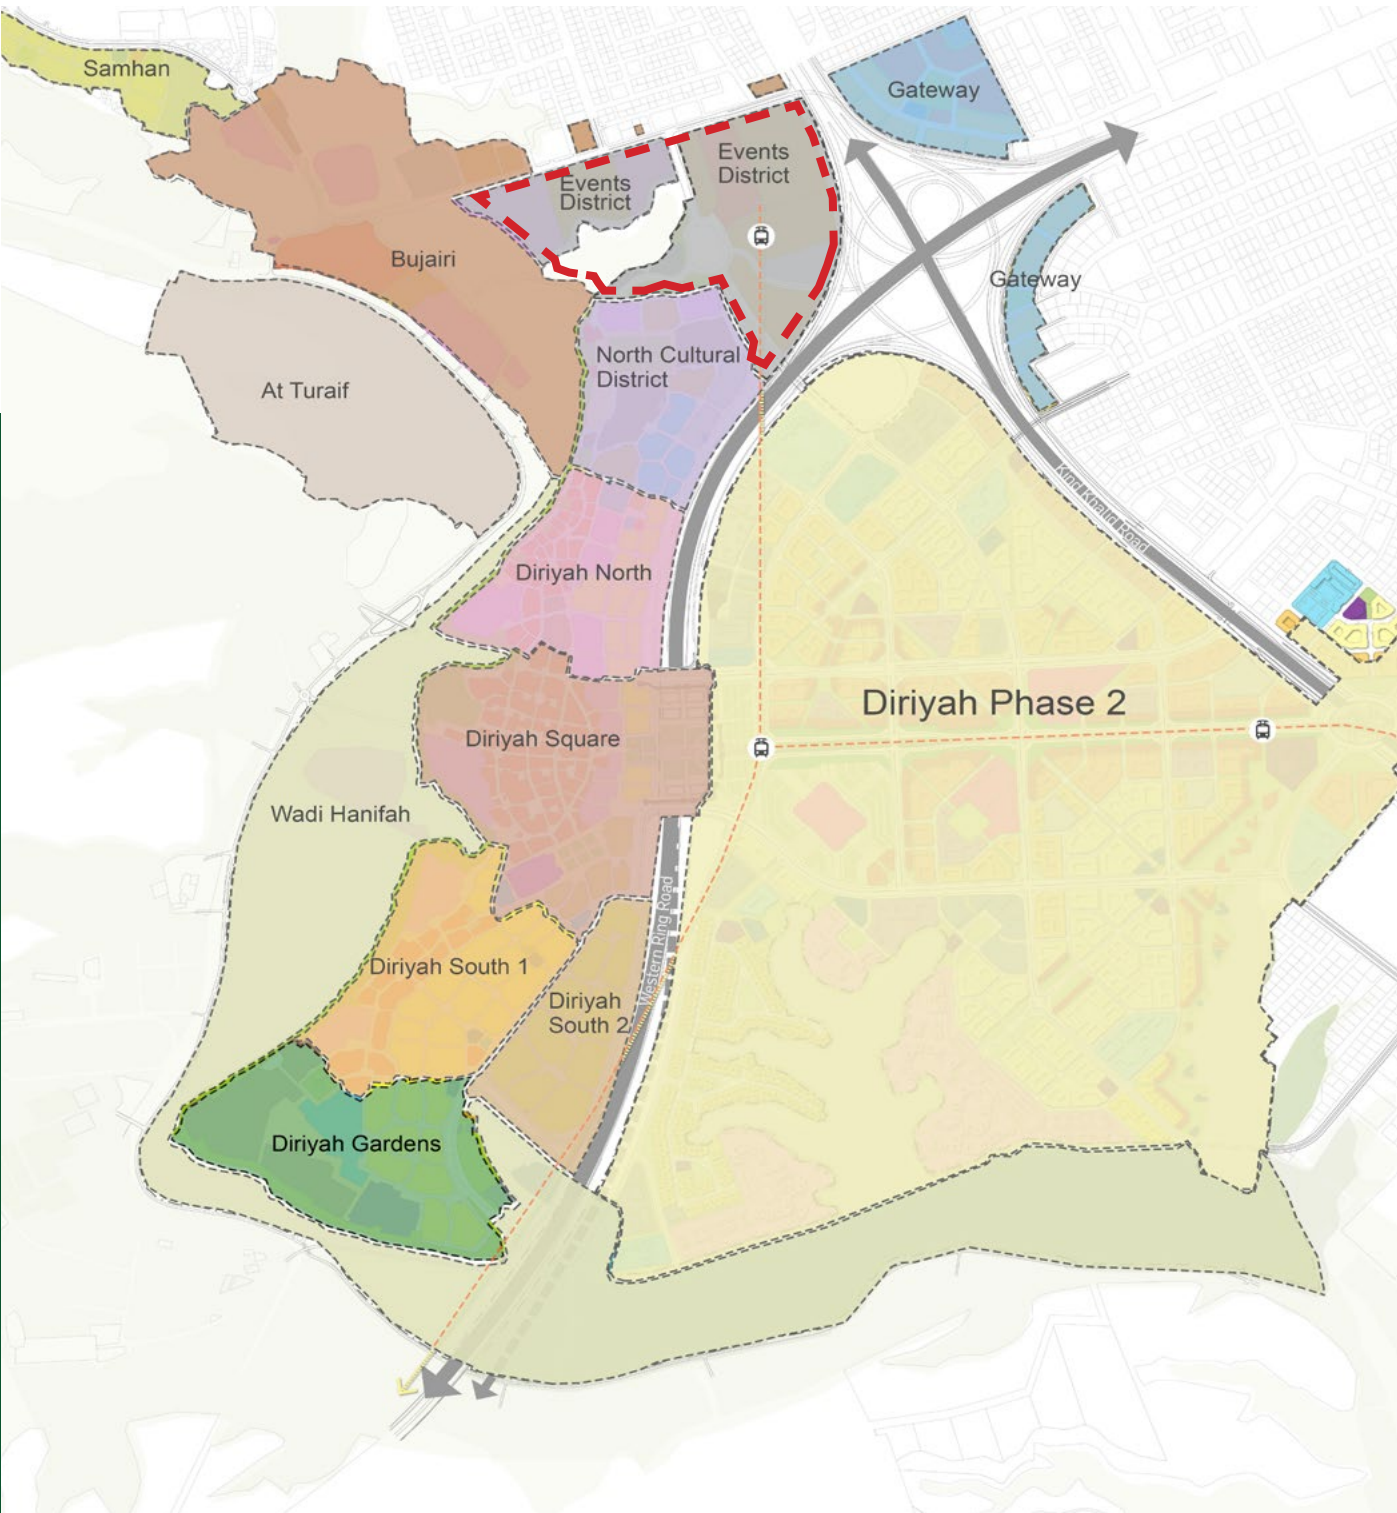

The Urban Design Strategy for the Southern Districts Master Plan is in line with the overall Master Plan structure and is defined by the following design parameters:

-  **Southern Key Node:** Diriyah Gardens is one of the 3 Key nodes identified in the Diriyah Gate 1 Urban Design Framework complement by the other two nodes: Northern Cultural District and Diriyah Square located north of these districts
-  **Pedestrian Spines:** The main element of the urban design strategy is a key pedestrian route that runs from the north to south which integrated the key nodes within Diriyah Gate 1.
-  **Public Realm Anchors:** The Islamic garden in Diriyah Gardens is the primary anchor complimented with plazas in Diriyah South Community and Diriyah Gardens West.
-  **Landmarks:** Given the scale of the development and limited height across the site a number of human scale landmarks shall be developed that can be appreciated by their grandeur and arrival experience.
-  **Views and Vistas:** The vistas and routes within the development are punctuated with structures of character with special height (taking inspiration from traditional fortresses) and landscape features which create unique interest points within the public realm.
-  **Escarpment Walk:** An Escarpment walk has been planned along the ridge towards Wadi Hanifah to maximize views to the Wadi and At-Turaif.
-  **Community Hubs:** A central community hub is planned with Diriyah South 1 to create a central gathering space for residents in the residential communities. This is complemented with central plazas within the residential clusters.

KEY OFFERINGS

-  **4 KEY DISTRICTS**
-  **2 ICONIC PLAZAS**
-  **1 KM LONG PEDESTRIAN SPINE THROUGH THE URBAN FABRIC**
-  **370 HOTEL KEYS CATERING TO A VARIETY OF TOURISTS**
-  **917 RESIDENTIAL UNITS CAN HOUSE 4,703 RESIDENTS**
-  **108,011 SQM OF OFFICE GFA**
-  **9,400 SQM OF DESTINATION, NEIGHBOURHOOD AND CONVENIENCE RETAIL**

3.2 Site Access & Connectivity

P2 area is strategically located at the intersection of major roads and provides excellent commercial visibility. Planned road and intersection upgrades are expected to facilitate the ability of customers.

Access to P2 is provided at two levels, at grade and subterranean level. The space as a whole should be carefully designed to be highly accessible and enhance the connectivity between various areas, creating an inviting atmosphere through thoughtful design of the public realm.

Access and engineering services to the P2 site are covered under a separate package and will be provided to the appointed consultant. The P2 Consultant will need to ensure compliance to these specialist studies and requirements as it relates to access points, vehicle stacking distances, utility connection points and capacity etc. Gating strategy and access strategy during events and in normal days shall also be developed by the consultants. On grade Pick up & Drop off locations are essential elements of the development's function. It must be developed carefully in order to enhance the user experience and to avoid any hindrances in operations Principles of PUDO & Servicing Strategy of Diriyah.

The following principles must be followed when developing the PUDO strategy for various modes:

1. Align with Master Plan vision to limit ongrade vehicular access to the business park and promote walkability.
2. Coordinate with the below grade carpark drop off and circulation
3. Maximise use of the parking structures for car/taxi PUDO to reduce the vehicular movement ongrade
4. Provide a minimum of two ongrade drop off that can serve the Valet parking and VIP access. The ongrade drop must be linked to the below grade carpark for an easy valet operation.
5. Provide sufficient plot infrastructure connections and access.
6. Adapt relevant design guidelines and development controls for the masterplan ad plot

The P2 South Business Park is accessed ongrade from the main road to the west through an internal road surrounding the Events District, and from the east connected to the main road, and from the basement level of Car Park through a welcome hall to the building. The space as a whole should be carefully designed to be highly accessible and enhance the connectivity between various areas. This in order to create an inviting atmosphere by the careful design of the public realm.

3.3 Bridge and Connectivity

The pedestrian bridge will serve as a connection between the P2 South Business Park Carpark and Diriyah Northern Cultural District (NCD) public realm located adjacent to the MOC HQ. The bridge will span over the upgraded Prince Sattam Road and will stand as an iconic landmark at the entrance to Diriyah Gate enhancing the visual charm of the area. The bridge design should reflect the traditional Najdi language of the development and stand as an iconic Najdi bridge. Its primary purpose is to provide a functional and secure passage for MoC staff during the week days, but also for pedestrians and cyclists by ensuring a smooth and efficient transition. To ensure accessibility for all users, the bridge will incorporate required vertical transportations such as lifts, travelators, and escalators. The enclosed, climate controlled bridge will be designed to create a visually stunning structure that complements the local context and adds a distinctive architectural element to the area (traditional Najdi). The design will carefully consider the surrounding environment, taking into account the architectural style, materials, levels, and color palette of the adjacent structures. The bridge's design will not only harmonize with its surroundings but also enhance the visual appeal of the area.

Incorporating public art installations or artistic features into the bridge design will provide visitors with a visually and culturally captivating design. The design elements will be thoughtfully sensitive to the local cultural context embedded within the Diriyah Gate masterplan. The overall design of the bridge will respect and reflect the cultural heritage, blending harmoniously with the surrounding environment.

Connecting buildings (welcome halls)

The bridge design scope includes the connecting parts/structures on both sides of development (within the P2 South Business Park plot above the carpark through its main welcome hall) and NCD Public Realm through a welcome hall that will provide both access to the Ministry of Culture HQ and access to the public realm. This Welcome Hall will accommodate the landings and all vertical transportation elements.

2000 of the 3400 bays within the carpark are being developed for MoC, hence the bridge has to be sized to handle the traffic volume for morning staff arrivals as well as evening departures. Additionally, when the carpark is used after hours/weekends/public holidays, the bridge has to handle visitors to P2 and the Northern Cultural District. Design conformance to all Fire, Life and Safety requirements remain a prerequisite.



Wasla Bridge of D II



Wasla Bridge of D II



Public transport – Taxi, Bus and local infrastructure

The DGI master plan seeks to have minimal traffic at the grade level, being primarily a walking zone. The wider DGI campus is serviced by local bus routes that integrate into the broader Riyadh network. Further details can be found in the Diriyah Development Concept Master Plan Report Volumes.

Public transport – Metro

The closest metro station to the site is planned to be located in the P2 Interface land - located at northern boundary of the overall P2 site. A metro tunnel runs below the P2 site.

Building Staff Access

The main offices point of access for the staff is mainly through the carpark welcome halls at basement levels. The asset designer will need to ensure the offices lobbies allow for access control from the access point linked to the welcome hall. These capark welcome halls act as the 24/7 manned entrance for staff, access couriers and other small deliveries when the building is not open to the public.

Car – drop off, parking

The P2 South Business Park should include designated on grade drop-off areas to ensure convenient access for users. Most users are expected to self-park in the local basement parking facility, entering the P2 South Business Park directly from the basement level into the welcome hall. Other general parking will primarily be located in the area outlined in the Diriyah Gate Concept Master Plan Report Volumes. Additionally, valet parking services will be provided at the ongrade level.

The circulation plan enables users to move seamlessly within the buildings, with escalators and lifts designed to facilitate quick and efficient movement between the basement and grade levels. This approach ensures accessibility and accommodates large volumes of patrons effectively.

Pedestrian Access

The P2 South Business Park is anticipated to fit well inside the site, and as such careful consideration for the pedestrian and access to the remainder of the site, in supporting the building's function and fit with the surrounding environment.

Delivery/Service vehicle access

An on-grade serving strategy must be developed for the P2 South Business Park. The overall service strategy should respect the pedestrian approach and traditional urban and architecture language.

Loading areas have to be positioned correctly so as to allow efficient movement of equipment, furniture etc into and out of the site.

- Location of and service yards ongrade should be carefully considered and avoid having cross circulations with visitors.
- Temporary and permanent storage spaces for all at grade assets shall be considered and carefully placed.
- Service yards should service the at grade assets and shall accommodate the following and not limited to:
 - General building services areas - General storage areas
 - Loading/off-loading docks
 - Waste-collection facilities
 - Other necessary service area provisions

The locations and the number of service yards within the P2 shall be optimized so that they serve in an optimal way the overall design solutions for the at-grade assets and possible events.

VIP access

Controlled direct access to the project for VIP drop-off and collection, possibly in connection with limited valet parking is to be considered. The ability to adequately accommodate and welcome VIP's through the basement (B1) level entrance is highly preferable to provide the building user with flexibility in the use of the space depending on the anticipated protocol requirements.



Pre-concept Structure Plan WIP

3.4 Early Pre-Concept Master plan of the Events District

Historic Diriyah P2
Pre-Concept Master Plan





4.0 Design Requirements

4.1 General Planning



The consultant is expected to provide the following:

▪ Baseline/fixes

The objective of this task is to confirm all design parameters, constraints, fixes and technical input required by DC and other consultants. The consultants are expected to identify and confirm the development brief, all planning assumptions, utility demands, road capacities and open space requirements and site fixes. The outcome of this task is to produce an up-to-date baseline for the concept. This baseline will be coordinate with all discipline and shall be confirmed with DC.

▪ Master Plan compliance

During the development of the concept design for each asset, current version of master plan compliance report will be issued by the consultant to confirm overall compliance with the vision of the development and the controlling parameters.

4.1.1 Pedestrian and Cycling Strategy

To promote a more active lifestyle, a well-defined pedestrian and cycling network is proposed within Diriyah Development project as a whole to encourage people to walk and cycle and live a healthier lifestyle. The key transport principle in the Master Plan is a well-defined pedestrianized environment with-in the walked city to provide pedestrian access to most, if not all, assets.



4.1.2 Landscape and Public Realm (For the full area indicated in the scope limit plan)



The character and quality of the landscape architectural design are integral to achieving the overall vision for the Diriyah I development. The landscape and public realm design for P2 should consider the below:

1. Be fully aligned with the overall Landscape Framework, Vision and Narrative, Public Realm design principles, Place making and Sustainability strategies.
2. Establish a Placemaking Strategy for P2 and associated outdoor spaces, indicating contextual responses to view corridors, events, pedestrian movement approaches, universal accessibility, public facilities, environmental constraints, events, and micro-climactic comfort.
3. Materials selection and design shall consider sustainability strategy requirements. Usage of local and sustainably sourced materials is encouraged for all elements of the public realm, particularly hardscape.
4. Planting selection and design shall adhere to DGDA plant manual principles (with predominantly native species supplemented with adaptive species only at instances, as required to achieve the Vision).
5. Design of all external public spaces shall be fully compliant with Universal Access Standards – as set in the approved Codes and Basis of Design – and walking (and cycling, where applicable) shall be preferred modes of travel within the development.
6. Outdoor Thermal Comfort strategy shall form an integral part of the design of all outdoor spaces, with provision of shading fully aligned with Mostadam and LEED requirements.
7. Key movement routes and connections with wider masterplan to function in both the permanent and temporary use scenarios.
8. Programmatic flexibility in the landscape design required. This may include strategies for removal of turf modules or flooring protection systems allowing spatial change of use for event use.
9. Fixed and modular furniture components shall both be represented allowing for the flexibility in design and functionality.
10. Utility provision/connections within public realm design to allow a 'plug and play' nature for event use and function.
11. Sympathetic designs solutions with a Najdi-fied approach to infrastructure elements shall ameliorate their presence in the public realm.
12. Programmatic landscape overlay to be considered for uses within 'cooler months' of October to March. In addition to the activities that will take place during the evenings and public holidays.
13. Landscape screening treatments either fixed or mobile to be included to filter and screen views towards event spaces when not in use.

4.1.3 Safety and Security

Security designs for all projects in Diriyah Development are to follow the DC security master planning and guidance documents in order to protect the public interest in a unified and coordinated manner. Early adoption of security planning and design guidance will ensure that projects result in a safe and secure built environment.

The overarching principles are:

- Security is to be embedded from the earliest stages and is to be coordinated with all relevant design disciplines to achieve an appropriate balance between architectural design and security measures.
- Security will be proportionate and appropriate to the project, using a risk-based approach. The security design is to be aligned with the overall DGI Masterplan, including the DGI Design Control Regulations and Safety and Security Guidelines.
- The security design should address relevant regulations that will shape security on the project.
- The principles of Crime Prevention Through Environmental Design (CPTED) are to be adopted in a project specific context.

- The various user groups expected in the project are to be identified (e.g. VIP's, residents, staff, etc.) and user journeys through security are to be addressed in the design.
- Where vehicle denial and hostile vehicle mitigation (HVM) is required, alternative measures should be considered such as landscape, street furniture or alternative solutions.
- Security should be designed with adaptability and scalability to accommodate business as usual, events and heightened threat scenarios allowing the security posture to change as necessary to accommodate the sites events.
- The security approach needs to support this principle.

4.1.4 Environment and Sustainability

The Diriyah Development Sustainability Vision statement is:

“To create a world class destination for visitors and locals alike within the Kingdom of Saudi Arabia that is renowned for being a resource efficient development which is resilient to climate change, promotes cultural heritage, high quality of life, and leading environmental performance.”

A Diriyah Development masterplan reflects the national sustainability vision and global sustainability megatrends, especially including Saudi National Vision 2030, Saudi Green Initiatives, PIF sustainability strategy, UN SDG, and Paris Agreement. A sustainable development strategy for P2 shall be developed with a clearly structured sustainability framework for the vision statement, objectives, targets, and KPIs.

Each master plan of Diriyah I, Diriyah II, and Diriyah III targets to achieve the highest designation (at the minimum Gold) in the LEED Cities and Communities as well as Mostadam for Community certifications.

P2 must contribute to the site-wide certifications and comply with any relevant requirements related to P2 design and development. Considerations should be provided to designing the site and assets in an environmentally sustainable manner. Items such as water conservation, lighting, orientation and outdoor thermal comfort strategies that reduce unnecessary energy and water wastage and utilizing open spaces and natural lighting efficiently amongst other items should be considered and recommendations provided.

The consultant shall achieve a target of 30% reduction in energy consumption.

P2 assets shall target to achieve LEED and Mostadam certifications at a minimum Gold level.

4.1.5 Smart Cities

By way of a mandate across all giga projects in KSA, there is a requirement for new developments to incorporate Smart City technology to ensure a seamless user experience and to provide city managed services to be optimized and perform with enhanced levels of efficiency. Smart City applications will ensure that the DC development can monitor, manage, and protect precious natural resources, including energy and water resources. Diriyah Development aspires to be a leading global innovator in the space of future/smart cities as a tourism and heritage destination with sustainability and a “human centric” approach.

The DL Smart City allows for optimized security system management, from surveillance to access control and will also provide support for life critical services. Public realm services include digital signage and wayfinding as well as applications such as smart parking, smart lighting, environmental monitoring and smart waste collection. There will also be applications that provide an intuitive user interface for residents, workers, and visitors to the development.

A Smart City platform will be incorporated into the development to aggregate city systems and sub-system data, and designers will be required to adhere to our Smart City requirements and will also be encouraged to promote applications suitable to their development area.

In order to achieve the above, a Smart City Strategy will be provided to align with the DC-wide strategy.



5.0 Above Grade Requirements

5.1 Introduction

The P2 South Business park forms part of Zone A of P2 where the below envisaged to provide 2,000 parking bays to the Ministry of Culture Head Office and the remaining 1,400 bays to be used primarily by the above grade offices. During off peak periods, these bays were all available for visitors to the events area.



5.2 Above Grade requirements

5.2.1 Commercial Offices and F&B

The focus of this document is the pedestrian bridge and above grade Commercial Offices including Retail/F&B located above the carpark in P2 South business park. The office areas make up the dominant use for business park above grade structures, accounting for approximately 44,000m2GFA and 3,000m2 of F&B/convenience retail, developed over three above-grade levels (Ground+3).

The P2 South Commercial Offices envisions the provision of Grade A Office space, a high-quality office development that offer modern, well-designed layouts, top-tier amenities, and high-quality finishes. The below table forms the basis of the design elements which differentiates between A Grade and B Grade space in the region and are to be used in the calibration of the final product outcome from a design perspective.

Grade	Grade A	Grade B+ / Grade B
Building Systems	- Includes air conditioning system not less than 2 pipe or similar system - Modern high-speed lifts, 30 seconds waiting time - Separate goods lift	- Includes air conditioning system not less than 2 pipe or similar system - Modern high-speed lifts, 45 seconds waiting time - Separate goods lift
Building Structure	- Includes suspended ceilings - Metal tiled - Includes tiled raised floor with compartmental floor boxes - Includes finished floor-to-ceiling height with suspended ceilings 2.7 m or greater with 1.5 m gross RAF allowance - Full height fenestration - Open efficient floor plates	- Includes suspended ceilings - Metal tiled - Includes tiled raised floor with compartmental floor boxes - Not full height fenestration but good natural light
Location & Accessibility	- Situated in a good location within its submarket - Good access	- Situated in a good location within its submarket - Good access
Parking	- Secured/covered parking (1:50 sqm or better) - Disabled parking allowance - Surface visitor parking	- Underground parking - Disabled parking allowance
Property Management & Services	Professional Property Management Services	Professional Property Management Services

Number of buildings: 4 buildings.

Consultant shall evaluate and propose connections between the building as an option for a singular tenant during the concept design stage and reviewed to provide tenancy for a single user (potentially bridges between buildings). In such case, the lift cores should be as close as possible to the bridges and levels differences between floor plates must be studied.



Project Components

South Business Park Commercial Offices will include the following:

- Front of House
 - Landscaping within boundary
 - VVIP on grade drop off
- Back of House
 - Loading Dock / Waste Management and Collection Area
 - Back-of-House Staff Support Facilities
 - General Administration Offices
 - Building Services Area

For these cases the designer must submit a deviations report as part of the concept design submissions highlighting all the deviations, mitigations against any impacts and confirming alignment and compliance with below-grade Car Park design and the master plan.

Ground Floor

- Each building will have its lobby on the ground floor. Each lobby will include:
 - Reception arrival;
 - Waiting lounge.
- The use of high ceilings is encouraged in the arrival hall and main reception areas
- Back-of-house areas shall be enclosed and facilitate general functions and services, related to the management of the asset
- Restrooms M / F should be provided in close proximity to the main entrance waiting areas;
- Allowance for the tenant to create additional prayers / ablution facilities.
- One office building could potentially be considered for an office center and/or provide flexible office working options (e.g. WeWork).

Upper floors

Each offices floorplate should have:

- Access to a terrace;
- Allowance for tearoom, printers room, additional restrooms (If required);
- Lettable office areas shall have the potential to accommodate open plan office layout, office
- Layout with individual offices, and a mixed plan layout (open plan areas and individual offices combination).
- Fenestration and access to daylight should be studied

Rooftop terrace

The offices will have line of sight to the landmark. Rooftop terraces should be developed to take advantage of these views.
The Consultant is also to review options of whether a view corridor to At Turaif is possible.

5.2.2 Spatial Program (Indicative)

Consultant should accommodate for 44,000 sqm of offices and 3,000 sqm off F&B and retail. The target, minimum efficiency ratio (GLA/GFA) will be based on the final tenant profile.
- 90% in case of single tenancy
- 80% in case of multi-tenancy

The next table indicate the typical functions and areas used for another offices project in DC. This must be used as the bases and consultant should demonstrate how the targeted efficiency is achieved through the design development.

As Employer, DC reserves the right to revise the brief during the design stages, in order to align the project and any of its component with the final Diriyah Development Masterplan, amended project development brief and business plan of the project.

For clear height requirements and detail breakdown please follow the below table. More detail can be found on the Retail RDD guidelines part of the starter package.

South Business Park Commercial Offices

Offices space breakdown

Public Spaces
Entrance Lobbies
Gallery / Exhibit Space
Multifunctional Room
Sub Total Public Spaces

Offices
Enclosed Office – Chief (ca. 10m²)
Open Plan Workspaces (5.5 m²/workspace)
Sub Total Offices

Office Support Spaces
Cafeteria
Office Lounges/Relaxation Rooms/Break out Spaces (75 m² each)
Kitchenettes / Pantry Spaces (12 m²/each)
Small Meeting Rooms (2 4 persons – 10 m²/each)
Medium Meeting Rooms (6 10 persons – 20 m²/each)
Large Meeting Rooms (12 18 persons – 40 m²/each)
Resource Rooms (10 m²/each)
Archive Room
Sub Total Office Support Spaces

Complementary Spaces
Toilets & Prayer Rooms (incl. Ablution and shoe racks)
Service Provider Management Office
Service Provider Meeting Room
Cleaning & Hygiene Equipment Store
Equipment Store
Maintenance Store
Security Office
BMS
CCTV Room
Sub Total Complementary Spaces

Back of House
Other Storage Rooms
First Aid Room
Emergency Services Security / Control Room
Sub Total Back of House

Unassigned Areas
Circulation @ 15%
Technical Rooms
Sub Total Unassigned Spaces

Sunken Floor requirements					FFL to False ceiling				MEP zone (Tenant False ceiling to underside of the slab)			
	Retail	F&B	Offices (general)	Offices (toilets /kitchen/pantry)	Retail	F&B	Offices (general)	Offices (toilets /kitchen/pantry)	Retail	F&B	Offices (general)	Offices (toilets /kitchen/pantry)
Ground Floor	100	400	150	400	4500	4500	4500	4500	1100/1200	1100/1200	1100/1200	1100/1200
First Floor + upper floors	100	400	150	400	NA	NA	3100	3100	900/1000	900/1000	900/1000	900/1000



5.2.4 Bridge

Consultant to refer to bridge details on point 3.3 Pedestrian Bridge and Connectivity

5.2.5 GSM Towers

The tower's location, as specified, is strategically chosen to optimize network coverage while blending seamlessly with the local cultural heritage. The design constraint is to ensure that the tower not only functions effectively as a telecommunications structure but also respects and reflects the unique Najdi architectural style.

This involves incorporating key elements such as the use of mud brick and the distinctive Najdi ornamentation, allowing the tower to stand as a modern tribute to the region's historical and cultural identity.


Further details on GSM Tower can be found in the starter package.

5.2.6 Connectivity between above grade & below grade assets:

The design of the building must align with the pre-established layout and infrastructure of the underground car park, which was developed by Jacobs. This car park already includes strategically positioned welcome halls and MEP (Mechanical, Electrical, and Plumbing) facilities to support its operation. As a result, the building's design should integrate seamlessly with these existing elements to ensure functionality, efficiency, and user convenience. Adapting the design to the car park's infrastructure will optimize circulation, facilitate service connections, and enhance the overall user experience by leveraging the groundwork already in place.

The car park is designed with three distinct entrances to ensure optimal accessibility and efficient traffic flow for users. The first entrance is at grade level from King Khalid Branch Road, providing direct access for vehicles approaching from the east. The second entrance, also at grade level, is located on Prince Sattam Road, catering to traffic from the north. The third entrance connects at the B2 level from the Western Ring Road, offering a convenient entry point for vehicles coming from the South.



The consultant scope includes integrating the welcome halls of the carpark and all carpark related popups as part of the above grade design. This includes careful consideration and design to the welcome hall facade and roof elements to reflect coordinated integrating masses.

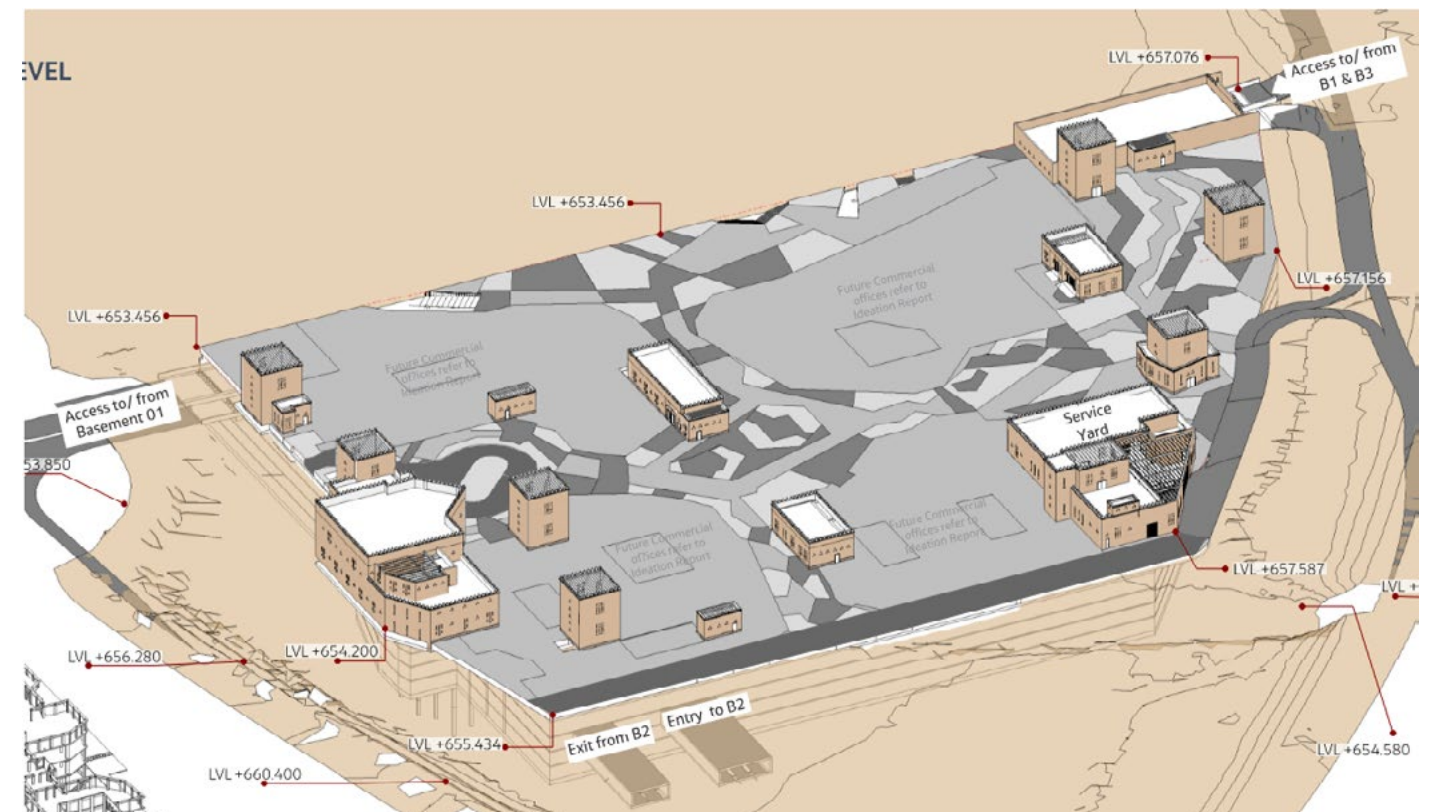

Based on the provided data, the car park features a capacity of 3,400 bays distributed over four levels, with essential support facilities, including four welcome halls, MEP and back-of-house (BOH) services, and a 1,000 m² facility management office. Above-grade elements include amenities, drop-off areas, VIP drop-offs, service yards, and fire egress points, ensuring efficient functionality. The total built-up area spans 161,775 m², divided into parking (148,005 m²), circulation (6,274 m²), useable areas (2,495 m²), and services (5,001 m²). This design balances operational efficiency with user convenience.

Consultant must refer to the carpark constraint package (Part of the starter package for the full constraint details)

Consultant should review and validate the constraint package before starting the concept design development.

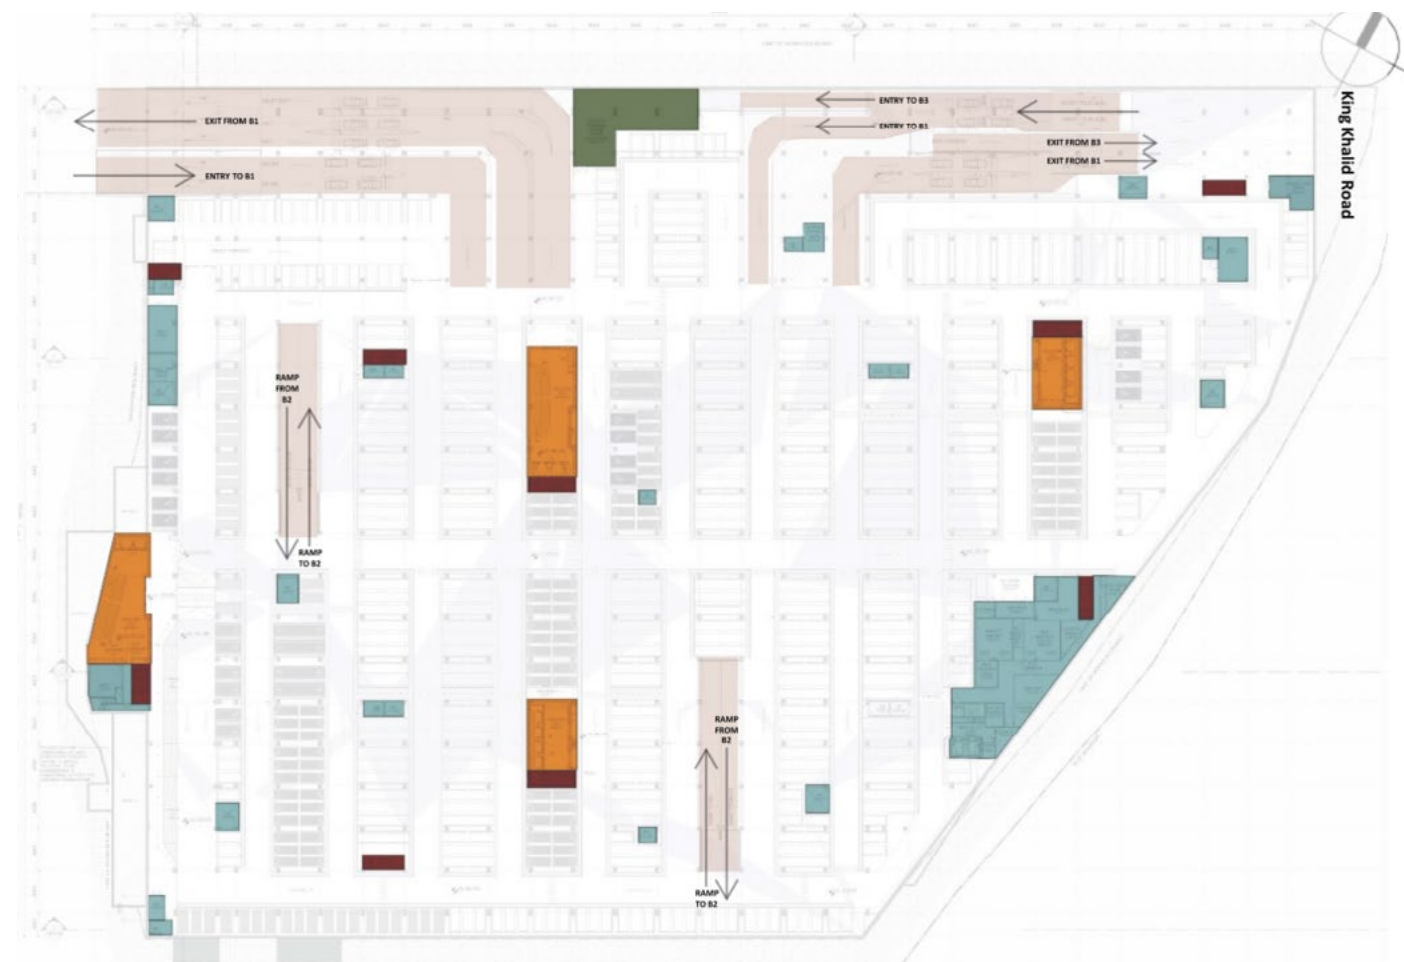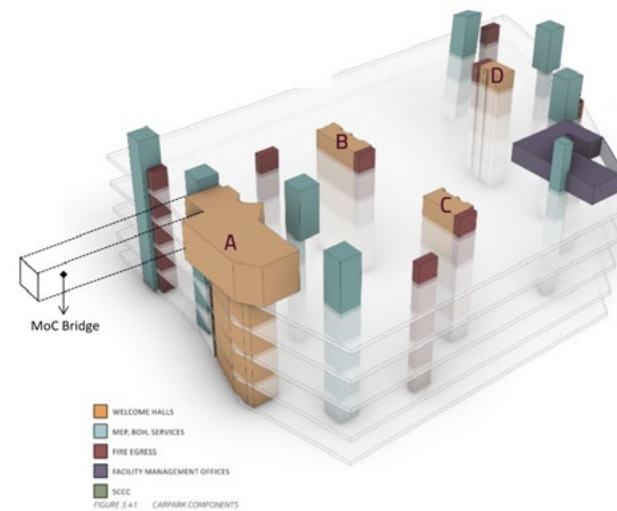

Basment 01

6.0 Design Considerations

6.1 Key Considerations

- Visitor's arrival experience by various modes of transportation is a key, and shall be integrated into the district in a convincing and seamless fashion, to promote P2 South business Park as a key destination and a gateway within the Diriyah project.
- Consideration of visitors and VIP customer arrival journey and experiences from above grade (direct access)
- Outdoor spaces shading shall be optimized, especially in high value pedestrian areas and zones, to ensure comfort at peak visitor time.
- Spatial and functional relation and transition to adjacent assets shall be carefully considered to provide convenient links and positive experiences through pleasant outdoor spaces, retail & building frontage activation.
- Considering the pivotal location of the P2 site relative to other Diriyah Development phases, the designer needs to consider the main entrance features that guests/ visitors will encounter on arrival. This has to be Najdi inspired, memorable and timeless in design.

Design the space considering a unique and grand journey experience for the visitors coming on grade access, the below grade access from the metro station, and pedestrians...etc.

The building should adhere to DC traditional Najdi language and specification reflected, where the internalized courtyards and sikka will provide an international standard of daylight penetration to the occupied spaces whilst creating the tightly woven intricate fabric of a traditional Najdi village, The construction of the exterior walls will be built by using CMU block and mud render to achieve the traditional look and feel.


The office building, being located above a parking basement, will be well connected by road and pedestrian links to the surrounding community.



6.2 Architectural Language

The architectural asset within the development is intended to showcase the history of Saudi Arabia through an engaging and inspiring set of cultural, educational entertainment and shopping experiences functionally incorporated into the authentic heritage inspired urban fabric and architectural style.

The architectural vision for Diriyah Development is a key component in ensuring the wider project vision is achieved. To this end, the entire development on the Western Plateau is envisaged to look and feel like At-Turaif in its prime around 300 years ago. The urban scale of At-Turaif, distinctive architectural character and unique palette of materials and colors are emulated in the Master Plan vision for Diriyah Development to achieve the Najdi authenticity and to revive the distinctive character of this UNESCO World Heritage site.

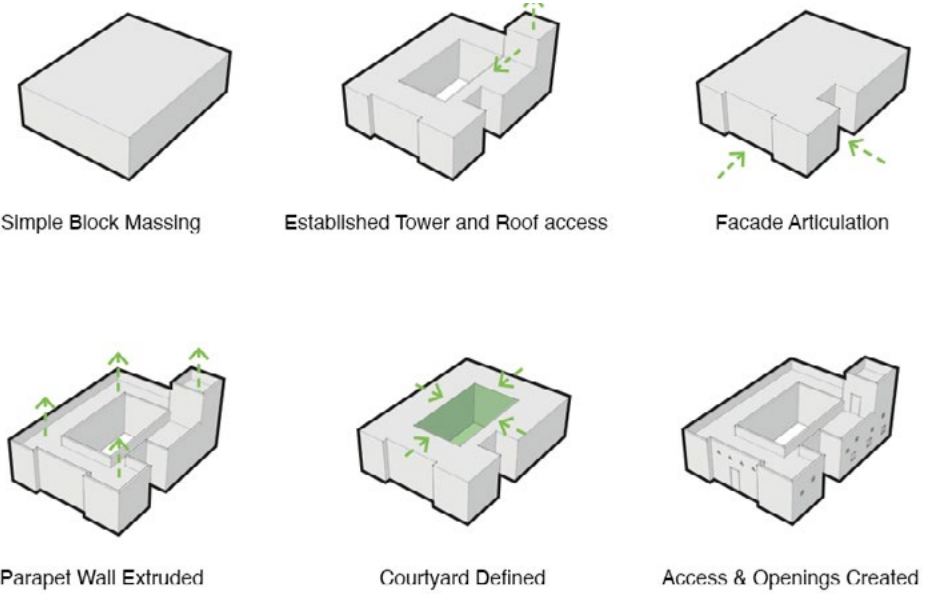


Organic in form

The Najd vernacular massing is a simple, low rise block of relatively irregular shape.


Building Articulation

Articulation is commonly applied within traditional Najdi architecture as well as a number of different variations across façades and building footprints.

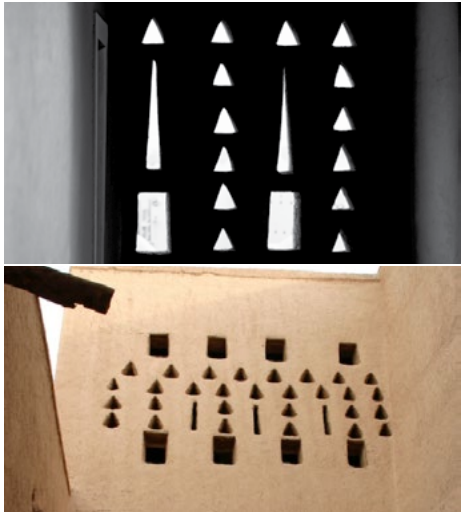

Small Openings

Small opening were arranged on the exterior walls to allow air circulation to the court while maintaining privacy.

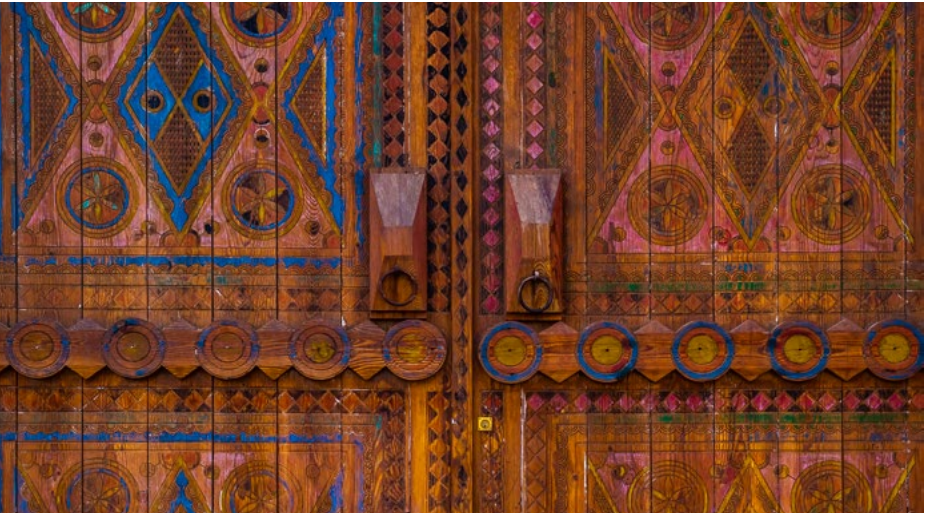

Decorated Doors

Doors encapsulate the delicate balance of privacy achieved by Najdi architecture. They are carefully positioned so as not to face those of a neighbor, whilst their painted geometric designs provide a hint of the rich family contained within.




Roofscape

All roof tops in Najd are generally flat and usually accessible from central courtyards.



Central Activated Courtyards

Buildings are generally arranged around courtyards that act as lungs of the houses to regulate the micro- climate.

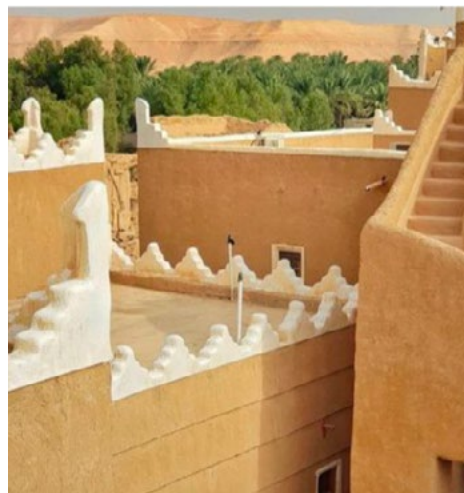

Roof tops & Crenellations

Saw tooth parapet walls also known as 'Sharfat' provides privacy for family members, allowing them to utilize the roofs for gathering purposes.



Building height variations

In order to achieve the overall "look and feel" of a traditional Najdi neighborhood, designers are to vary storey heights between buildings to create vertical interest in the masterplan.

6.3 Vertical Transportation

Access from the car park to ground floor is mainly through the designed four welcome halls connecting 4 levels of carpark with the ground level. consultant to refer to constraints package for full details.

Access from ground floor to upper floors:

- Common lift lobby with to serve each above grade floor.
- Number and size of lifts to be confirmed through traffic studies (minimum 2 lifts per buildings).

The lift lobby at each above grade floor will give access to:

- Restrooms M/ F (small, based on average occupancy);
- A small terrace and access to daylight from the lift lobby;
- MEP rooms / cabinets;
- Emergency/fire stair shall be provided from basement to the ground floor lobby and all above grade floors;
- Stairs design should encourage its usage by workers;
- Access to daylight and/or to open terraces should be addressed as key design consideration.

6.4 Structure

A loading schedule has been prepared for designing the foundation and columns of the underground carpark in order to accommodate the future development loads. This loading schedule is followed as per zoning layout reflected in the constraints package. Consultant to refer to constraints package part of the starter package for full structural constraints.

Structural Zoning Plan, please refer to 361 241219 HLL_South Business Park Constraints Draft.pdf



6.5 Radiant Cooling System

A Radiant Cooling System should be implemented in commercial office buildings and F&Bs, by respecting and reflecting the unique Najdi architectural style.

For further details on the radiant cooling system, including the proposed flooring detail, radiant cooling parameters, and public real design options, refer to the starter pack under Diriyah Square Radiant Cooling System.

Further details on Radiant Cooling Systems can be found in starter package.

6.6 Interior Design

It is recommended that the Architecture firm engage a offices specialist interior design firm. Considered instrumental to leaving a lasting and sophisticated impression on the guest experience, the interior journey within is to demonstrate these qualities:

- The interior design and planning is to relate to Najdi historical, cultural and social context, and are to and be inspired by local tradition and culture.
- The integration between interior and the exterior is to keep the visual communication open between the two.
- The interiors are to reflect ultra luxury finishes and spaces.
- The Welcoming Lobby experience is a key driver for the guests interior experience, and is to create an incredible first impression.
- The design is to primarily maintain and celebrate a reference to Najdi interiors. However the design team may re-interpret elements of Najdi traditions and culture, and the wider Arabian context, in items as finishes, furniture, art, artefacts, pattern, color, etc., through a contextual yet fresh approach.



6.7 Landscape Design

The character of the landscape proposal, and its plant species strategy, should respect the district specific landscape mood and guidelines.

- The landscape proposal should be designed to create a cohesive visual identity for the entire site and complement the surrounding context of the district.
- The design should be sensitive to the site's historical and cultural significance.
- The plant selection should be based on the specific microclimates and soil conditions of the site, ensuring their long-term viability and sustainability.
- The design should prioritize the use of drought-tolerant and low-maintenance plants to reduce water consumption and maintenance costs.
- The design should include strategies for managing stormwater runoff, such as bioswales and rain gardens.
- The landscape design should consider the needs of all users, including pedestrians, cyclists, and vehicles, and provide safe and accessible paths of travel throughout the site.
- Lighting should be integrated into the landscape design to ensure safe and attractive night-time use of the site.



6.8 Sustainability Strategy

The design shall comply with the following sustainability standards:

Rating System	Minimum Level
LEED BD+C	Gold
SITES	Gold, with an aspirational target of Platinum
MOSTADAM D+C	Gold

Note: The Design Team will consider the LEED / MOSTADAM certification goals mentioned above, deliver a design accordingly, and prepare a LEED / Mostadam scorecard identifying requirements.

In general, the following design features must be considered:

- Passive design strategies, insulated design, utilizing optimal building orientation and the use of natural lighting.
- Water conservation methods.
- Water recycling and reuse on site.
- Irrigation systems and strategies that minimize water loss.
- Utilization of grasses that minimize irrigation requirements.
- Environmental systems / habitat enhancement.
- Xeriscaping and native planting strategies.
- Green roofs and green walls.
- Energy usage efficiency overall, and specifically for irrigation systems and lighting.
- Renewable energy.
- The indoor environment, minimizing VOC's sources; use of recycled and recyclable materials, as well as regional materials.
- Utilizing all feasible WELL minimum requirements, with an aspirational target of Silver certification.



6.9 Safety & Security Requirements

Security designs for all projects in Diriyah Development are to follow the DC security master planning and guidance documents in order to protect the public interest in a unified and coordinated manner.

Early adoption of security planning and design guidance will ensure that projects in DG1 result in a safe and secure built environment.

In general, the following principles must be considered:

- Security is to be embedded in the design of P2 from the earliest stages and is to be coordinated with all relevant design disciplines to achieve an appropriate balance between architectural design and security measures.
- Security will be proportionate and appropriate to the project, using a risk-based approach. The security design is to be aligned with the overall DG1 Masterplan, including the DG1 Design Control Regulations and Safety and Security Guidelines.
- The security design should address relevant regulations that will shape security on the project.
- The principles of Crime Prevention Through Environmental Design (CPTED) are to be adopted in a project specific context.
- The various user groups expected in the project are to be identified (e.g. VIP's, residents, staff, etc.) and user journeys through security are to be addressed in the design.
- Where vehicle denial and hostile vehicle mitigation (HVM) is required, alternative measures should be considered such as landscape, street furniture or alternative solutions.
- Security should be designed with adaptability and scalability to accommodate both business as usual and heightened threat scenarios.

6.10 DC Guidelines

As part of Diriyah Development, the consultant must consider all applicable design and engineering guidelines shared as part of the starter package.



7.0 Design Programme & Milestones

Please refer to the programme included in the Procurement Strategy.



8.0 Appendix





8.1 Definitions

In this Schedule of Services, unless the context otherwise requires, the following capitalized words, if any, shall have the following meanings.

Terms	Definition
Authority Approval Strategy	Means the strategy produced by the Design Consultant and approved by the EMPLOYER, for the preparation, submission and obtaining of Local Authorities approvals and NOCs for the PROJECT.
Checklist	Means the tabulated Services and Deliverable as contained in this Design Brief.
Competition	Means the invited design competition organized by the Employer for the purpose of realizing the Diriyah Development Hotel project.
Competitor	Means the Architect participating in the design Competition.
Concept Design	Means the design produced by the Design Consultant.
Deliverable	Means the information and materials prepared by the Competitor in the performance of the services.
Design Guardianship	Means the services rendered by the Design Consultant to safeguard the design and vision of the winning competition entry, as approved by the Employer, during the subsequent design and construction stages.
Detailed Design	Means the design produced by the Multidisciplinary Consultant.
Design Consultant	Refers to the author of the winning Competition entry, who is appointed by the Employer successfully to carry out the services.
Design Parameters	Means the document of the same name prepared by the CONSULTANT and other CONSULTANT Team that defines all the design parameters and codes to be used in the design and describes all the design concepts to be incorporated in to the design based on the Employer’s requirements set out in the Project Brief.
Design Services	Means the design services as listed in this Design Brief, which form part of the services and to be performed in the stages as described in Scope of Work.
Gateway	Means the formal milestone and approval of the CONSULTANT information by the EMPLOYER at the end of each Stage.
Issued for Construction Documents or IFC Documents	Means the Tender Documents prepared, amended (if required) and issued to the Contractor for construction in accordance with the procedure set out in this Design Brief.
Multidisciplinary Consultant	Means the other consultant appointed by the Employer at the beginning of the Schematic Design stage to develop and deliver the detailed design of the project, inclusive of engineering.
Pre-Concept Design	Means the early conceptual design or competition entry produced by the CONSULTANT as more particularly described the in the Scope of Services section of the Brief.
Project Brief	Means the information and data representing the Employer requirements which are subject to periodic update.
Project Budget	Means the budget provided by the EMPLOYER for the PROJECT.
Project Quality Plan or PQP	Means the document of the same name governing the administration of the Consultant’s quality assurance processes and procedures in the performance of the Services.
Project Team	Means the entire team of consultants, sub-consultants, surveyors and specialists appointed by the EMPLOYER to provide consultancy and survey services for the PROJECT.
Sales & Marketing Information	Means the documents produced by the CONSULTANT for the EMPLOYER to use for the purpose of selling and marketing the PROJECT.
Schematic Design	Means the design produced by the CONSULTANT.
Tender	Means the finalization, management, coordination and preparation of Tender Documents, and issue of Tender Documents to tenderers, evaluation and awarding of the tender(s) for the construction works.

8.2 Abbreviations

In this Schedule of Services, unless the context otherwise requires, the following capitalized words, if any, shall have the following meanings.

CD	Civil Defence	FAR	Floor Area Ratio	PMS	Power Management System
DC	Diriyah Development Company Limited	FoH	Front of House	PoS	Point of Sale
GACA	General Authority for Civil Aviation	FF&E	Furniture, Fixtures & Equipment	PQP	Project Quality Plan
MOE	Ministry of Education	FTP	File Transfer Protocol	PT	Post Tensioned
MOI	Ministry of Interior	GRMS	Guestroom Management System	PTE	Pre-Tender Estimate
MOH	Ministry of Housing	GFA	Gross Floor Area	QA	Quality Assurance
MOMRA	Ministry of Municipal and Rural Affairs	GRP	Glass-fiber Reinforced Plastic	QC	Quality Control
MOT	Ministry of Transport	HOS	Head Office System	QS	Quantity Surveyor
NWC	National Water Company	H&S	Health & Safety	RC	Reinforced Concrete
QOL	Quality of Life	HVAC	Heating, Ventilation, Air Conditioning	RCP	Reflected Ceiling Plan
RCRC	Royal Commission of Riyadh City	IBC	International Building Code	RFP	Request For Proposal
SEC	Saudi Electrical Company	ID	Interior Design	SA	Saleable Area
AoR	Architect of Record	IDR	Interval Data Recorder	SMATV	Satellite Master Antenna TV
BMS	Building Management System	IFC	Issued For Construction	STP	Sewerage Treatment Plant
BoH	Back of House	LA	Leasable Area	TBC	To Be Confirmed
BoQ	Bills of Quantities	LOD	Level of Detail – BIM model	TSE	Treated Sewage Effluent
BUA	Built Up Area	LPG	Liquid Petroleum Gas	UKAS	United Kingdom Accreditation Service
CCTV	Closed Circuit TV	LTHW	Low Temperature Hot Water	UPS	Uninterruptible Power Supply
CGI	Computer Generated Imagery	MATV	Master Antenna TV	VAV	Variable Air Volume
CR	Commercial Registration	MCC	Motor Control Centre	VE	Value Engineering
CV	Curriculum Vitae	MD	Multi Disciplinary Consultant	VOC	Verification of Conformity
DB	Distribution Board	MDR	Maintenance Data Recorder	VR	Virtual Reality
DC	Document Control	MEP	Mechanical Electrical Plumbing	WBS	Work Breakdown Structure
DLP	Defects Liability Period		Medium Temperature Hot Water	SBC	Saudi Building Code
DMP	Design Management Plan	NOC	No Objection Certificate	LEED	Leadership in Energy and Environmental Design
EH&S	Environment, Health & Safety	O&M	Operations & Maintenance		
ELV	Extra Low Voltage	OS&E	Operators Supplies & Equipment		
ESD	Environmentally Sustainable Design	PABX	Private Automatic Branch Exchange		
		PCC	Process Control Centre		

8.3 Project Stakeholders

Terms	Definition
The “EMPLOYER” and their “REPRESENTATIVE”	Diriyah Development Company Limited (DC) (or their authorised representative).
The “CONSULTANT”	The party addressed by this RFP, and responsible for the delivery of the Services.
“Other consultants”	The party / parties assigned by the EMPLOYER for the delivery of Other Services in relation to the PROJECT.
“Sub-Consultant”	The party assigned by the CONSULTANT for the delivery of part of the Services.



8.4 Appendix 01 | Consultants Starter Pack

The documents listed in this section are attached to the Design Brief and considered part of it.

The consultants shall confirm receipt of all the enumerated files below.

S/N	Document name
1	DGI Master Plan Document and P2 Updated Pre-concept
2	Constraints Package
3	P2 South Business Park Plot (Scope)Limit AutoCad and PDF
4	P2 Ariel Photos and Videos
5	Diriyah Company Render Guidelines
6	RDD Development Brief
7	P2 South Business Park Plot
8	GSM Towers
9	Radiating Cooling System
10	Adobe Technical Documents
11	Concrete Mix Application
12	DG I Sustainability Starter Pack
13	DG1 Security Guidelines
14	FLS Guidelines
15	DG1 Signage & Wayfinding guidelines
16	DG1 Smart Cities guidelines and compliance check list
17	DG1 waste management strategy & design compliance checklist
18	Digital Delivery Pack BIM
19	Diriyah Offices Reference
20	Environmental Requirements
21	IT Guidelines
22	Measurement Requirements
23	MOC Boundary Wall Design
24	Public Realm Guidelines
25	GSM Tower Guidelines

